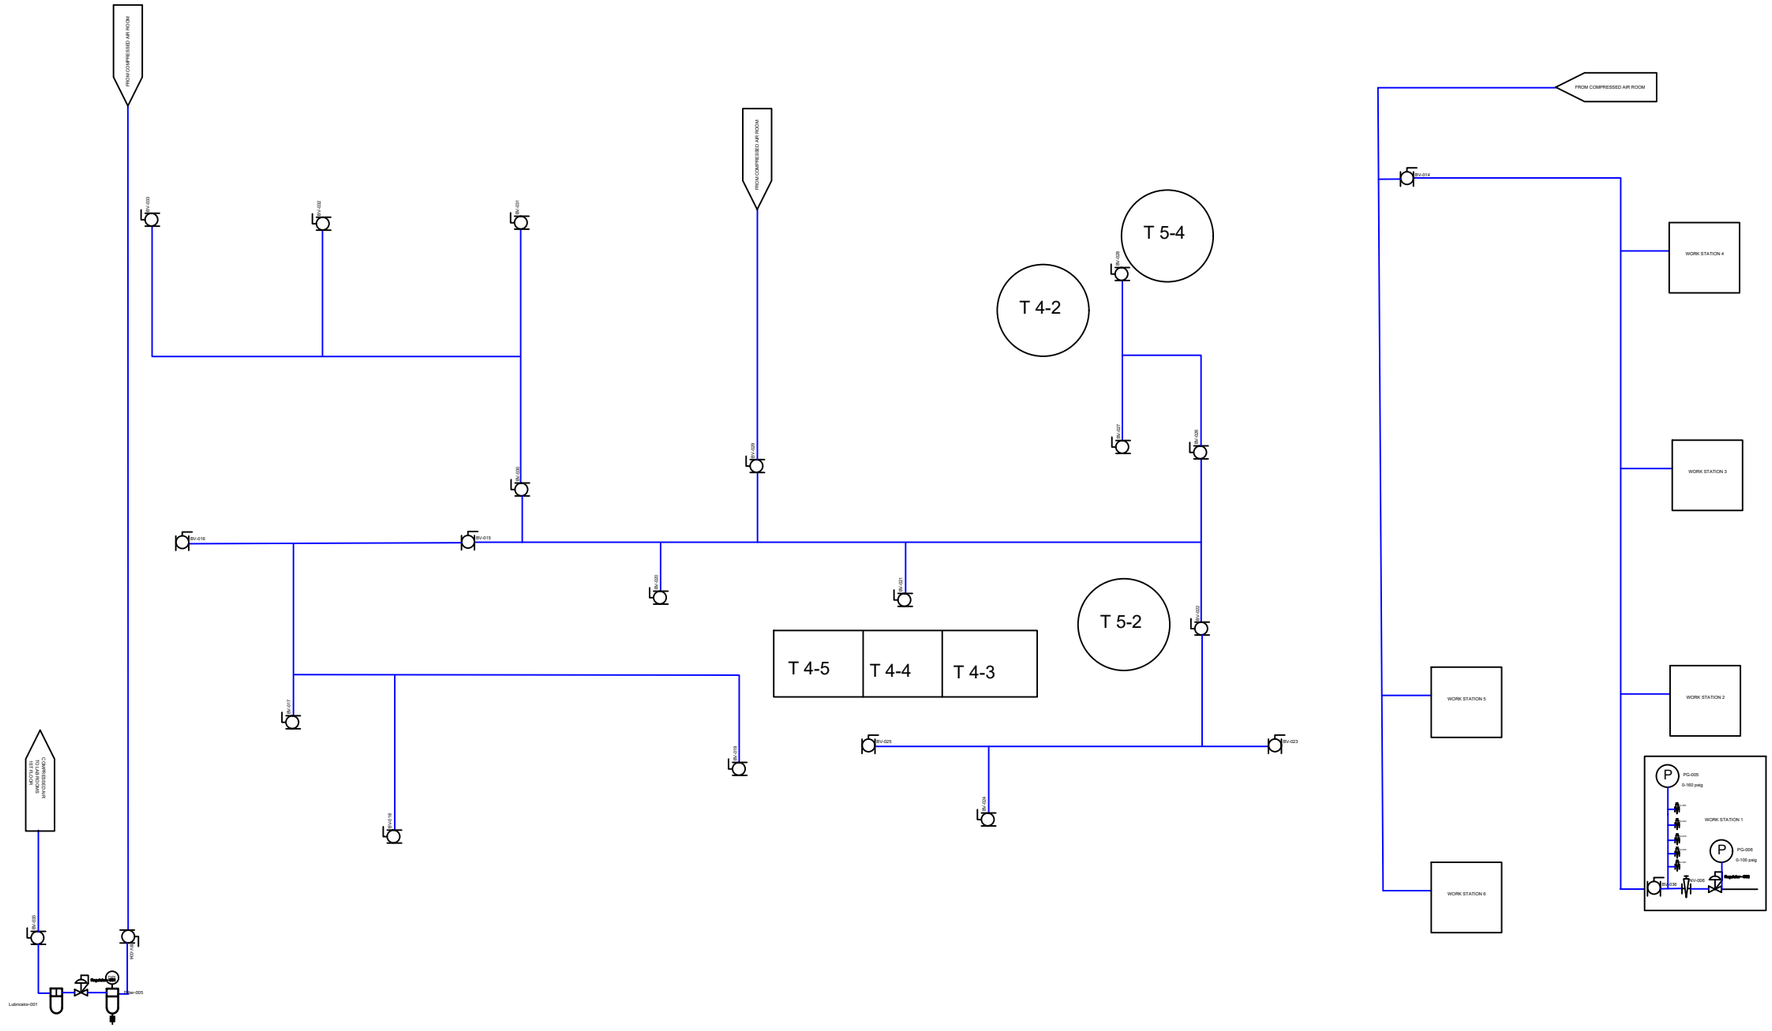


LEGENDS:

- GATE VALVE
- BALL VALVE
- CHECK VALVE
- FLOAT TRAP
- PISTON VALVE
- PRESSURE GAUGE
- FILTER WITH DIFFERENTIAL PRESSURE INDICATOR AND DRAIN VALVE
- PURGED AIR MUFFLER
- SOV-001
- 3 WAYS SOLENOID P/B AIR SWITCHING VALVE
- LUBRICATOR
- REGULATOR
- NEEDLE VALVE
- LOCAL CONTROL PANEL

COMPRESSED AIR DISTRIBUTION SYSTEM 1ST FLOOR SCALE:NTS

DRAWN: PH

11/27/2017