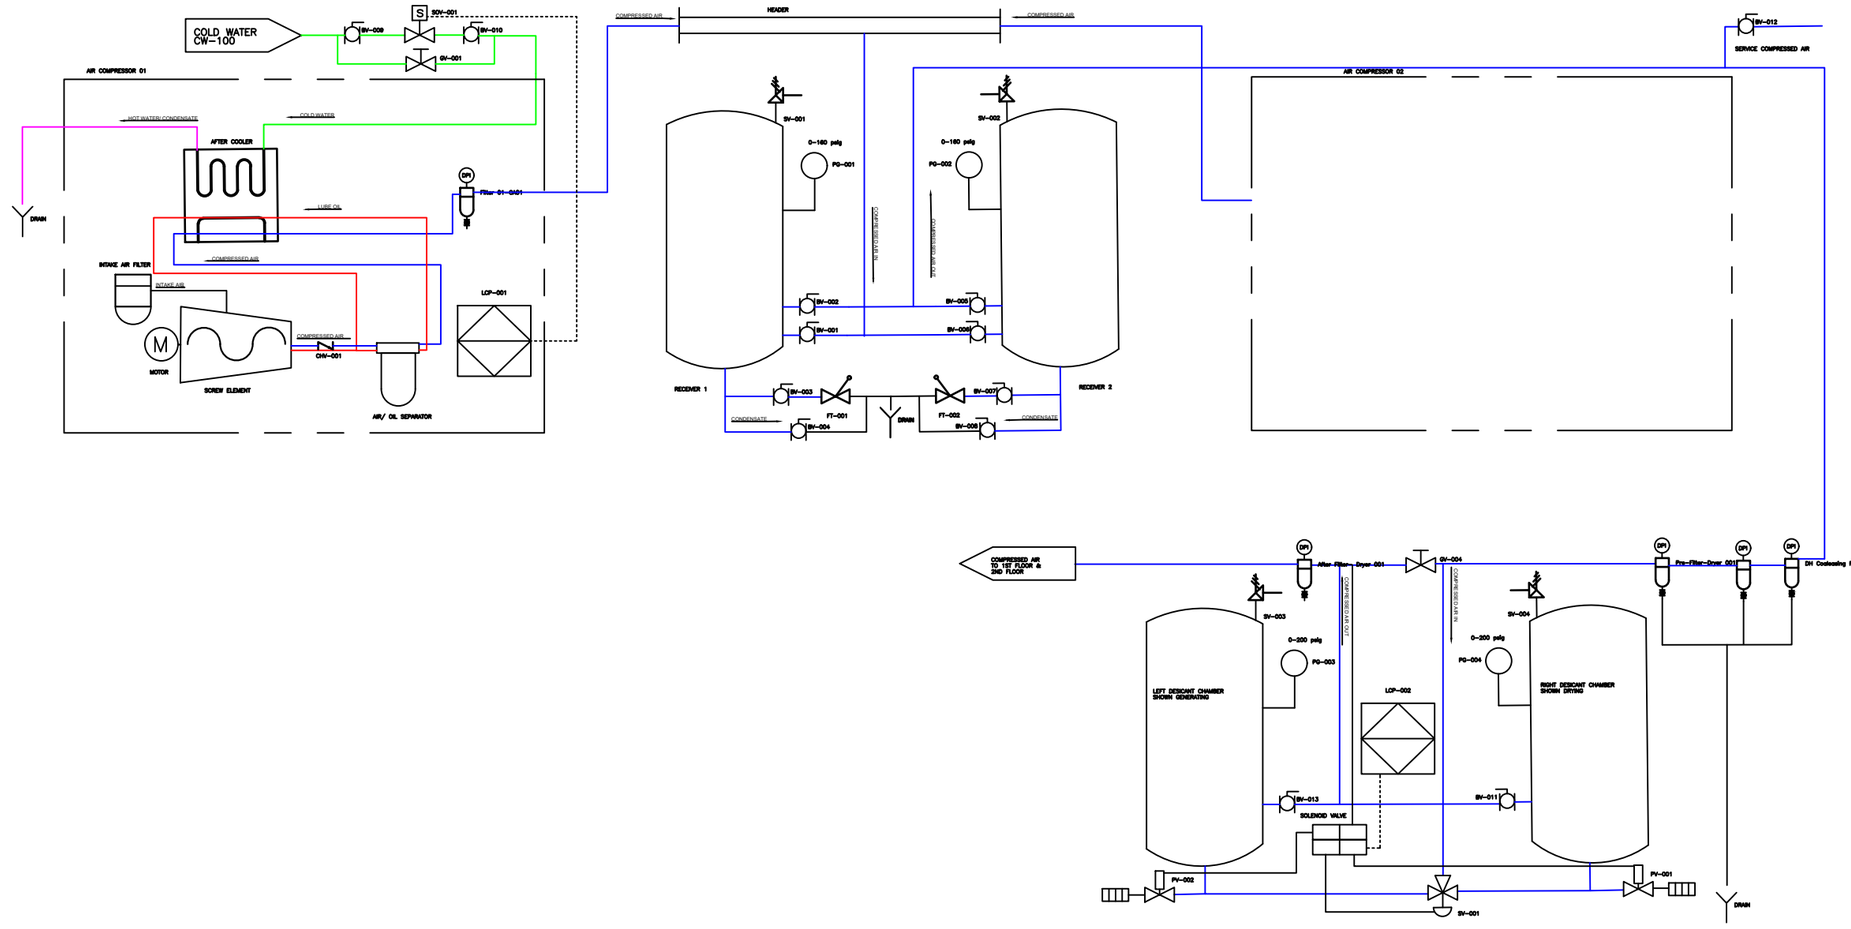


LEGENDS:

GATE VALVE
BALL VALVE
CHECK VALVE
FLOAT TRAP
PISTON VALVE
PRESSURE GAUGE
FILTER WITH DIFFERENTIAL PRESSURE INDICATOR AND DRAIN VALVE
PURGED AIR MUFFLER
SOV-001
3 WAYS SOLENOID PB AIR SWITCHING VALVE

COMPRESSED AIR ROOM P&ID

SCALE: NTS

DRAWN: PH

11/27/2017